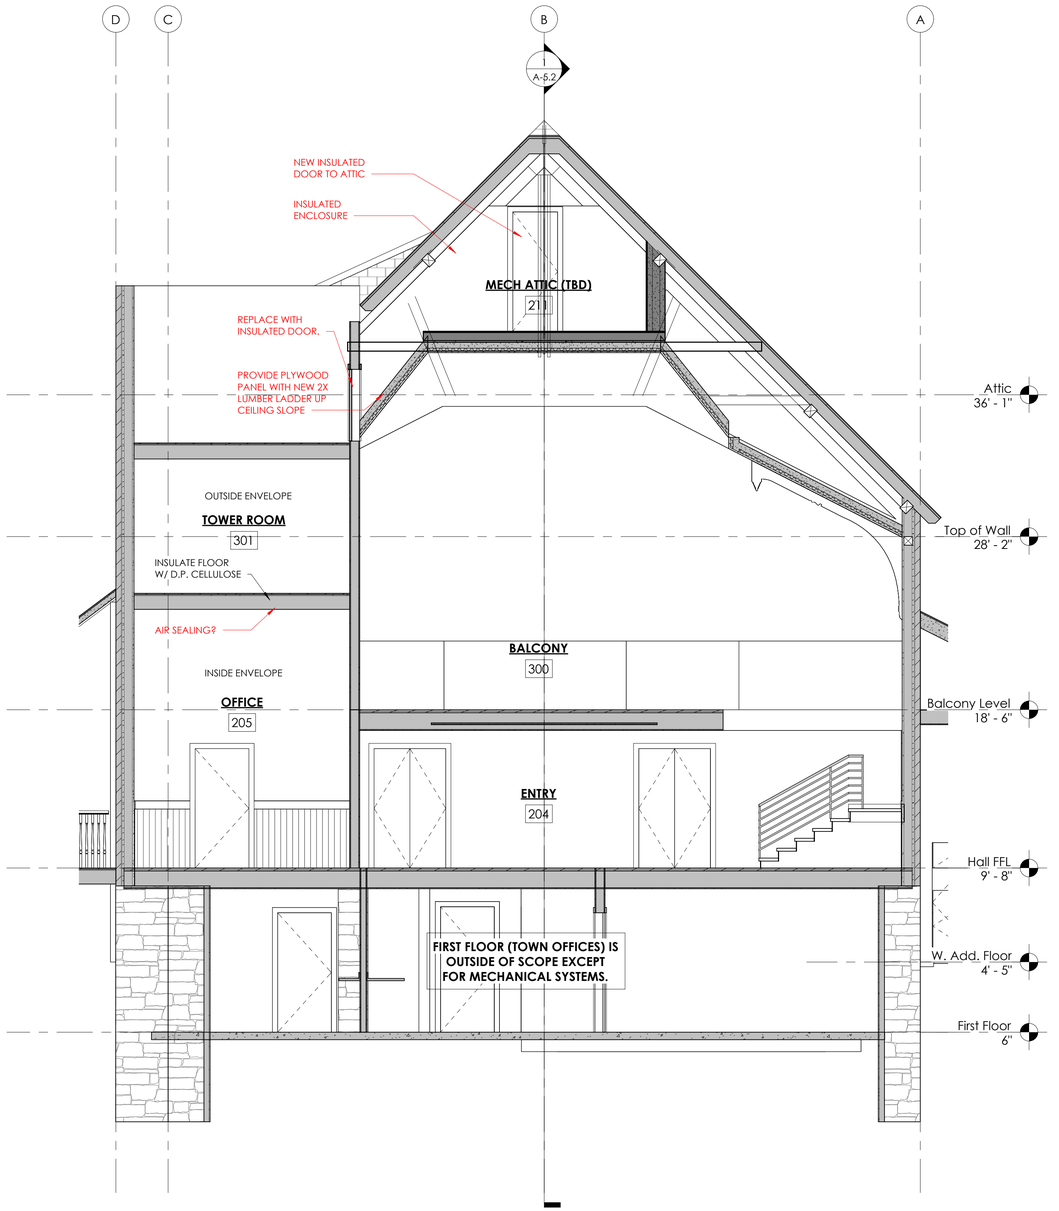


2 Cross Section at Mech. Attic and Tower
1/4" = 1'-0"

VERMONT INTEGRATED
ARCHITECTURE, PC

ANDREA MURRAY, AIA, NCARB, LEED AP
andrea@vermontintegratedarchitecture.com

ASHAR NELSON, AIA, LEED AP
ashar@vermontintegratedarchitecture.com

MEGAN NEDZINSKI, AIA, NCARB, LEED AP, CPHC
megan@vermontintegratedarchitecture.com

P.O. Box 862
Middlebury, VT 05753
802.989.7249

MEP ENGINEER
Nicholas Thiltgen, P.E., LEED AP
DuBois & King, Inc.
nthiltgen@dubois-king.com
802.728.7224

STRUCTURAL ENGINEER
Alex Horn, P.E.
Engineering Ventures, PC
alexh@engineeringventures.com
802.861.0267

DATE ISSUED: 9/29/25
Drawn: GB
Checked: NW

REVISIONS:

PRELIMINARY - NOT FOR CONSTRUCTION

BRISTOL ENERGY RESILIENCE PROJECTS
HOLLEY HALL

1 South Street,
Bristol,
VT 05443

CROSS SECTION

A-5.1