
SECTION DETAILS AND MATERIALS LEGEND

- WEATHER RESISTIVE BARRIER (WRB)/ DRAINAGE PLANE
- VAPOR CONTROL LAYER (VCL)
- AIR CONTROL LAYER (ACL)
- UNDER SLAB VAPOR CONTROL LAYER
- TAPE OR SELF ADHERING WATERPROOFING MEMBRANE (SAWM) AT EDGES/ JOINTS/ INTERSECTIONS


- CLOSED CELL SPRAY FOAM INSULATION
- RIGID FOAM INSULATION
- FILL INSULATION
- RIGID MINERAL WOOL INSULATION
- BATT INSULATION
- PLYWOOD
- STONE FILL
- EARTH
- CONCRETE
- WOOD FINISH GRADE
- DIMENSIONAL LUMBER
- BLOCKING

SECTION LEGEND


- DEMOLISH/REMOVE
- EXISTING TO REMAIN

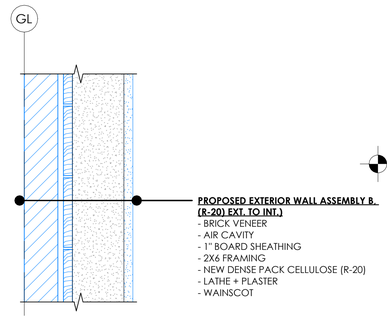


5 Typical Wall Section - Proposed Upgrade B
1 1/2" = 1'-0"

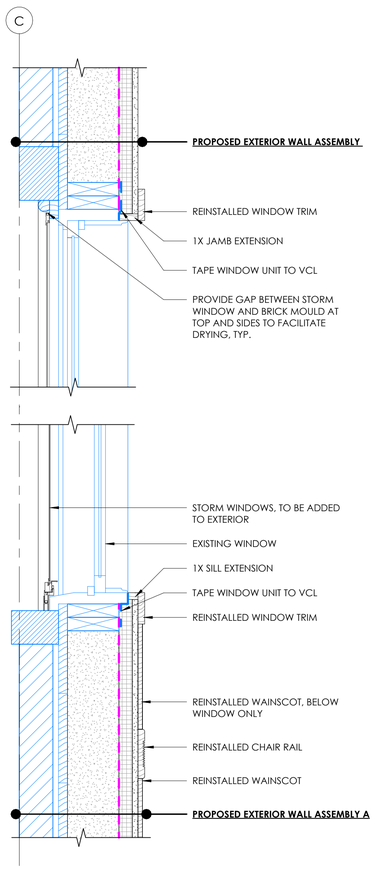


4 Typical Window Detail - Proposed Upgrade
1 1/2" = 1'-0"

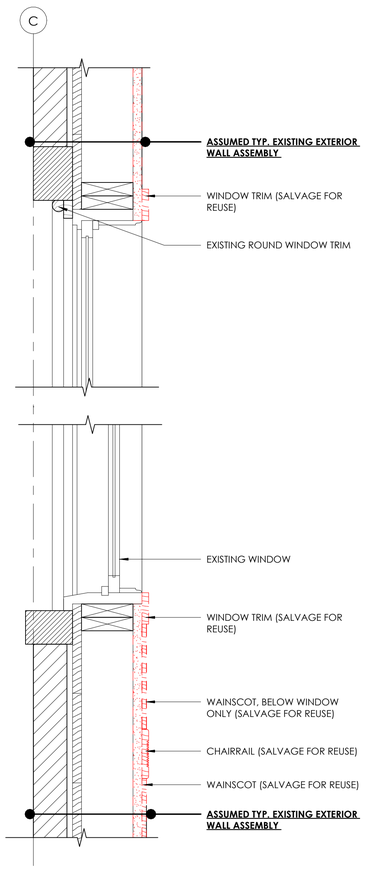

3 Typical Window Detail - Existing/Demo
1 1/2" = 1'-0"

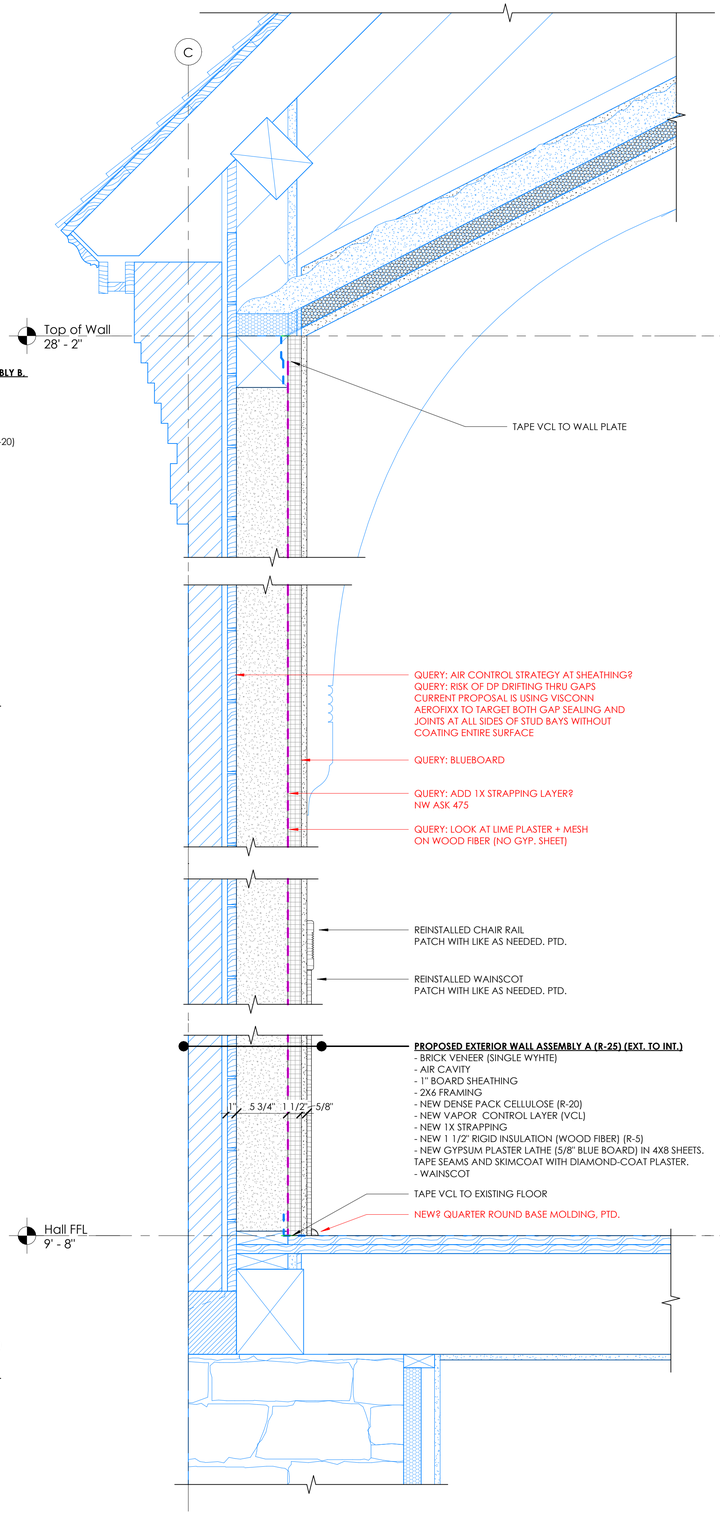

2 Typical Wall Section - Proposed Upgrade A
1 1/2" = 1'-0"

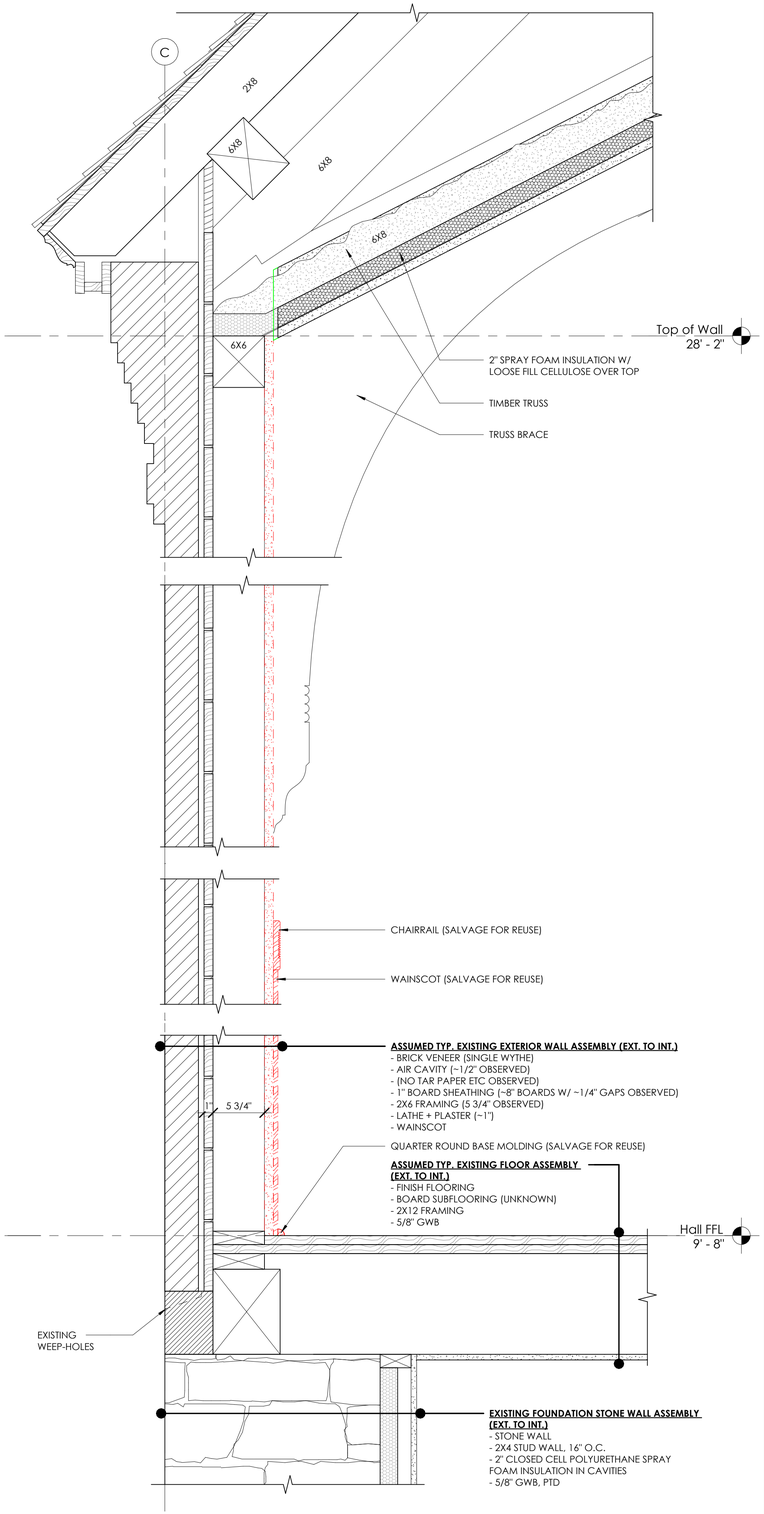

1 Typical Wall Section - Existing/Demo
1 1/2" = 1'-0"

VERMONT INTEGRATED
ARCHITECTURE, PC

ANDREA MURRAY, AIA, NCARB, LEED AP
andrea@vermontintegratedarchitecture.com

ASHAR NELSON, AIA, LEED AP
ashar@vermontintegratedarchitecture.com

MEGAN NEDZINSKI, AIA, NCARB, LEED AP, CPHC
megan@vermontintegratedarchitecture.com

P.O. Box 862
Middlebury, VT 05753
802.989.7249

MEP ENGINEER
Nicholas Thiltgen, P.E., LEED AP
DuBois & King, Inc.
nthiltgen@dubois-king.com
802.728.7224

STRUCTURAL ENGINEER
Alex Horn, P.E.
Engineering Ventures, PC
alexh@engineeringventures.com
802.861.0267

DATE ISSUED: 9/29/25
Drawn: GB
Checked: NW

REVISIONS:

PRELIMINARY - NOT FOR CONSTRUCTION

BRISTOL ENERGY RESILIENCE PROJECTS
HOLLEY HALL

1 South Street,
Bristol,
VT 05443

WALL SECTIONS

A-6.1

9/29/2025 3:16:07 PM