




CEILING AT BAY 2-3 C

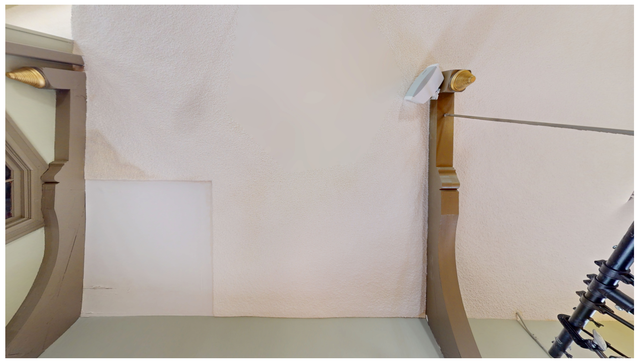

CEILING AT BAY 5-6 C
NOTE AREA WITHOUT SONASPRAY FINISH TO BE SHIMMED

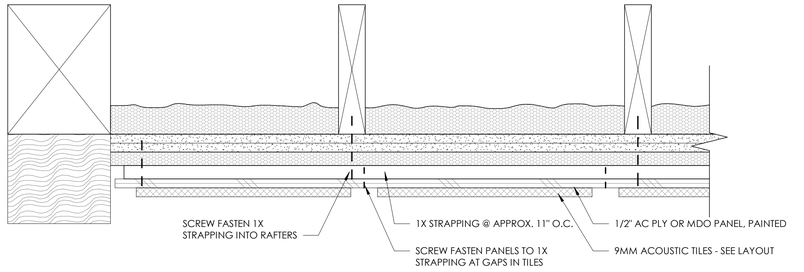

2 Section detail of panel mounting
3" = 1'-0"

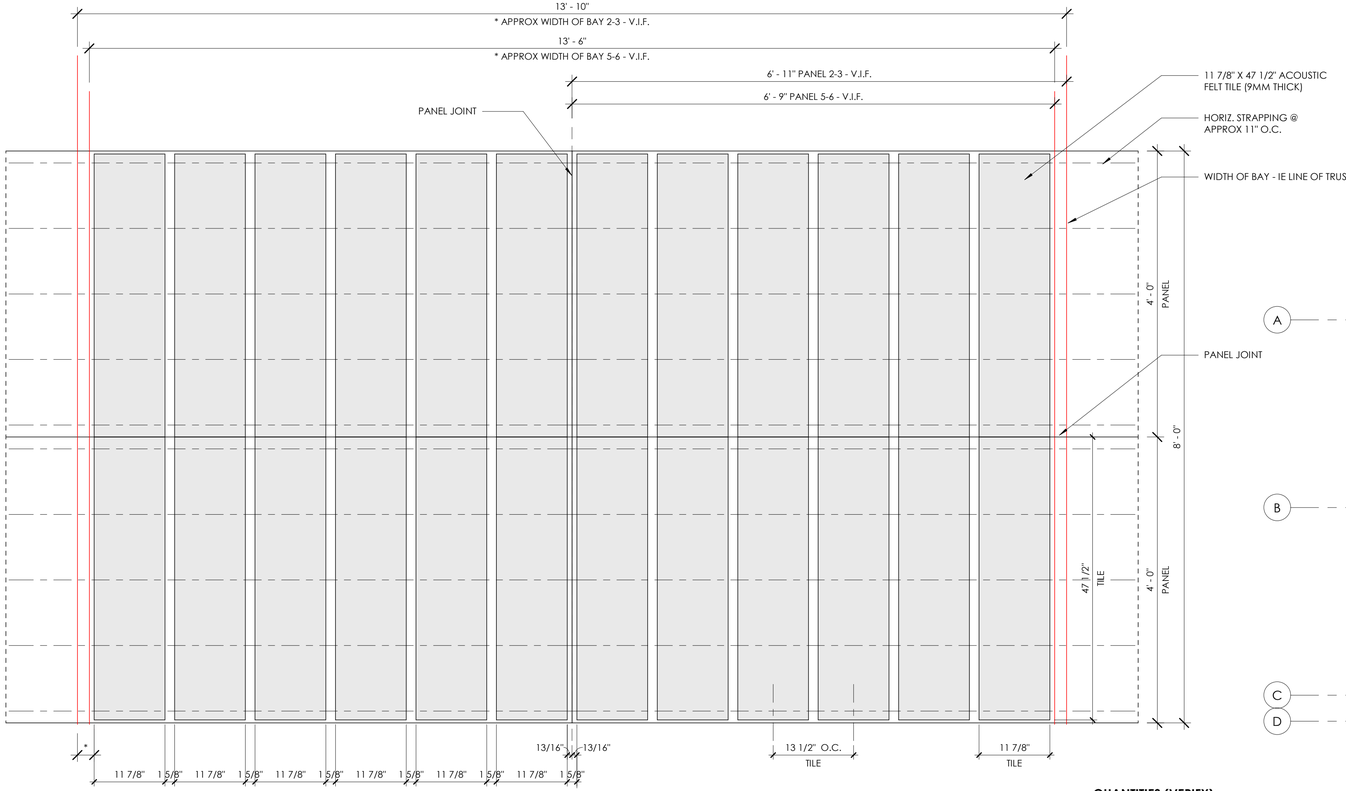


QUANTITIES (VERIFY):
6 TILES PER PANEL
4 PANELS PER BAY
24 TILES PER BAY
4 BAYS = 96 TILES

3 Panel Layout Diagram
1" = 1'-0"

NOTES:
- EACH BAY CONSISTS OF 4 PANELS WHICH CAN BE INDIVIDUALLY MOUNTED ON STRAPPING
- SEE APPROX. PANEL WIDTHS FOR LAYOUT WITHIN BAYS. VERIFY MEASUREMENTS
- CENTER ENTIRE ASSEMBLY AND TILE ARRAY WITHIN BAY, MAINTAIN EQUAL TILE SPACING EVERYWHERE.
- USE END OF PANELS TO ADJUST TO TOTAL WIDTH AT BAYS (THIS WIDTH VARIES BY A FEW INCHES)

TILE QUANTITIES (VERIFY):
- 6 TILES PER PANEL
- 4 PANELS PER BAY
- 24 TILES PER BAY
- 4 BAYS = 96 TILES
(ALLOW FOR WASTE)

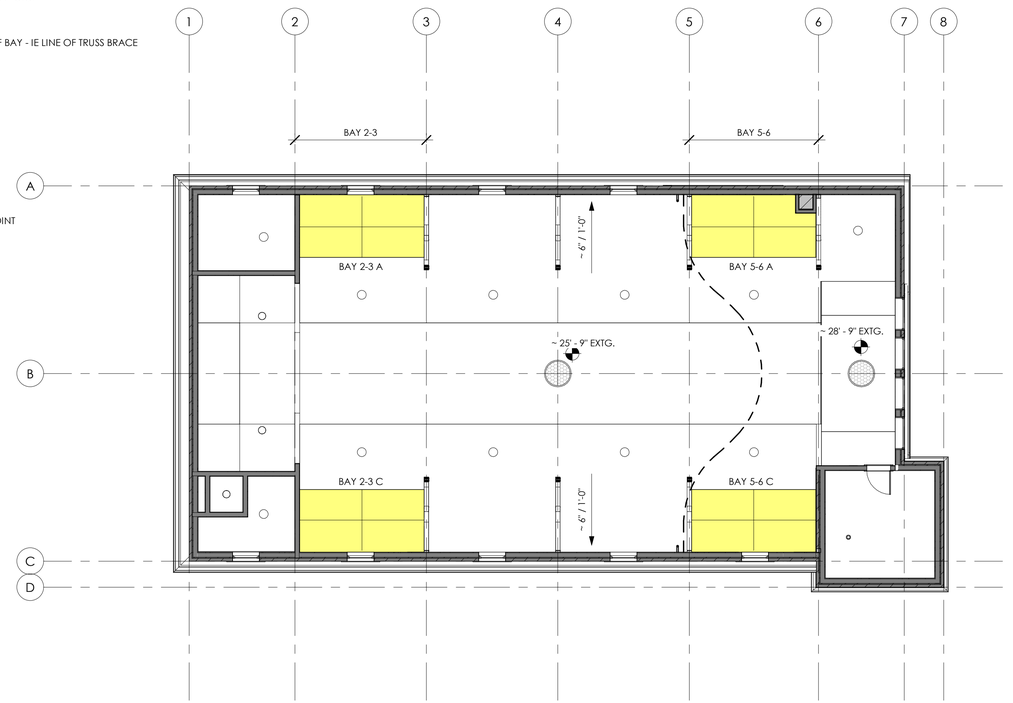

1 Reflected Ceiling Plan - Panel Location Plan
1/8" = 1'-0"

VERMONT INTEGRATED
ARCHITECTURE, PC

ANDREA MURRAY, AIA, NCARB, LEED AP
andrea@vermontintegratedarchitecture.com

ASHAR NELSON, AIA, LEED AP
ashar@vermontintegratedarchitecture.com

MEGAN NEDZINSKI, AIA, NCARB, LEED AP, CPHC
megan@vermontintegratedarchitecture.com

P.O. Box 862
Middlebury, VT 05753
802.989.7249

TYPE OF CONSULTANT
First Last
Company
email address
000.000.0000

LICENSED ARCHITECT
ASHAR NELSON
NO. 2695
STATE OF VERMONT

DATE ISSUED: 10/05/26
Drawn: NW
Checked: .

REVISIONS:

BRISTOL ENERGY RESILIENCE PROJECTS
HOLLEY HALL

1 South Street,
Bristol,
VT 05443

ACOUSTIC CEILING PANELS

A-7.3

10/5/2026 3:38:39 PM