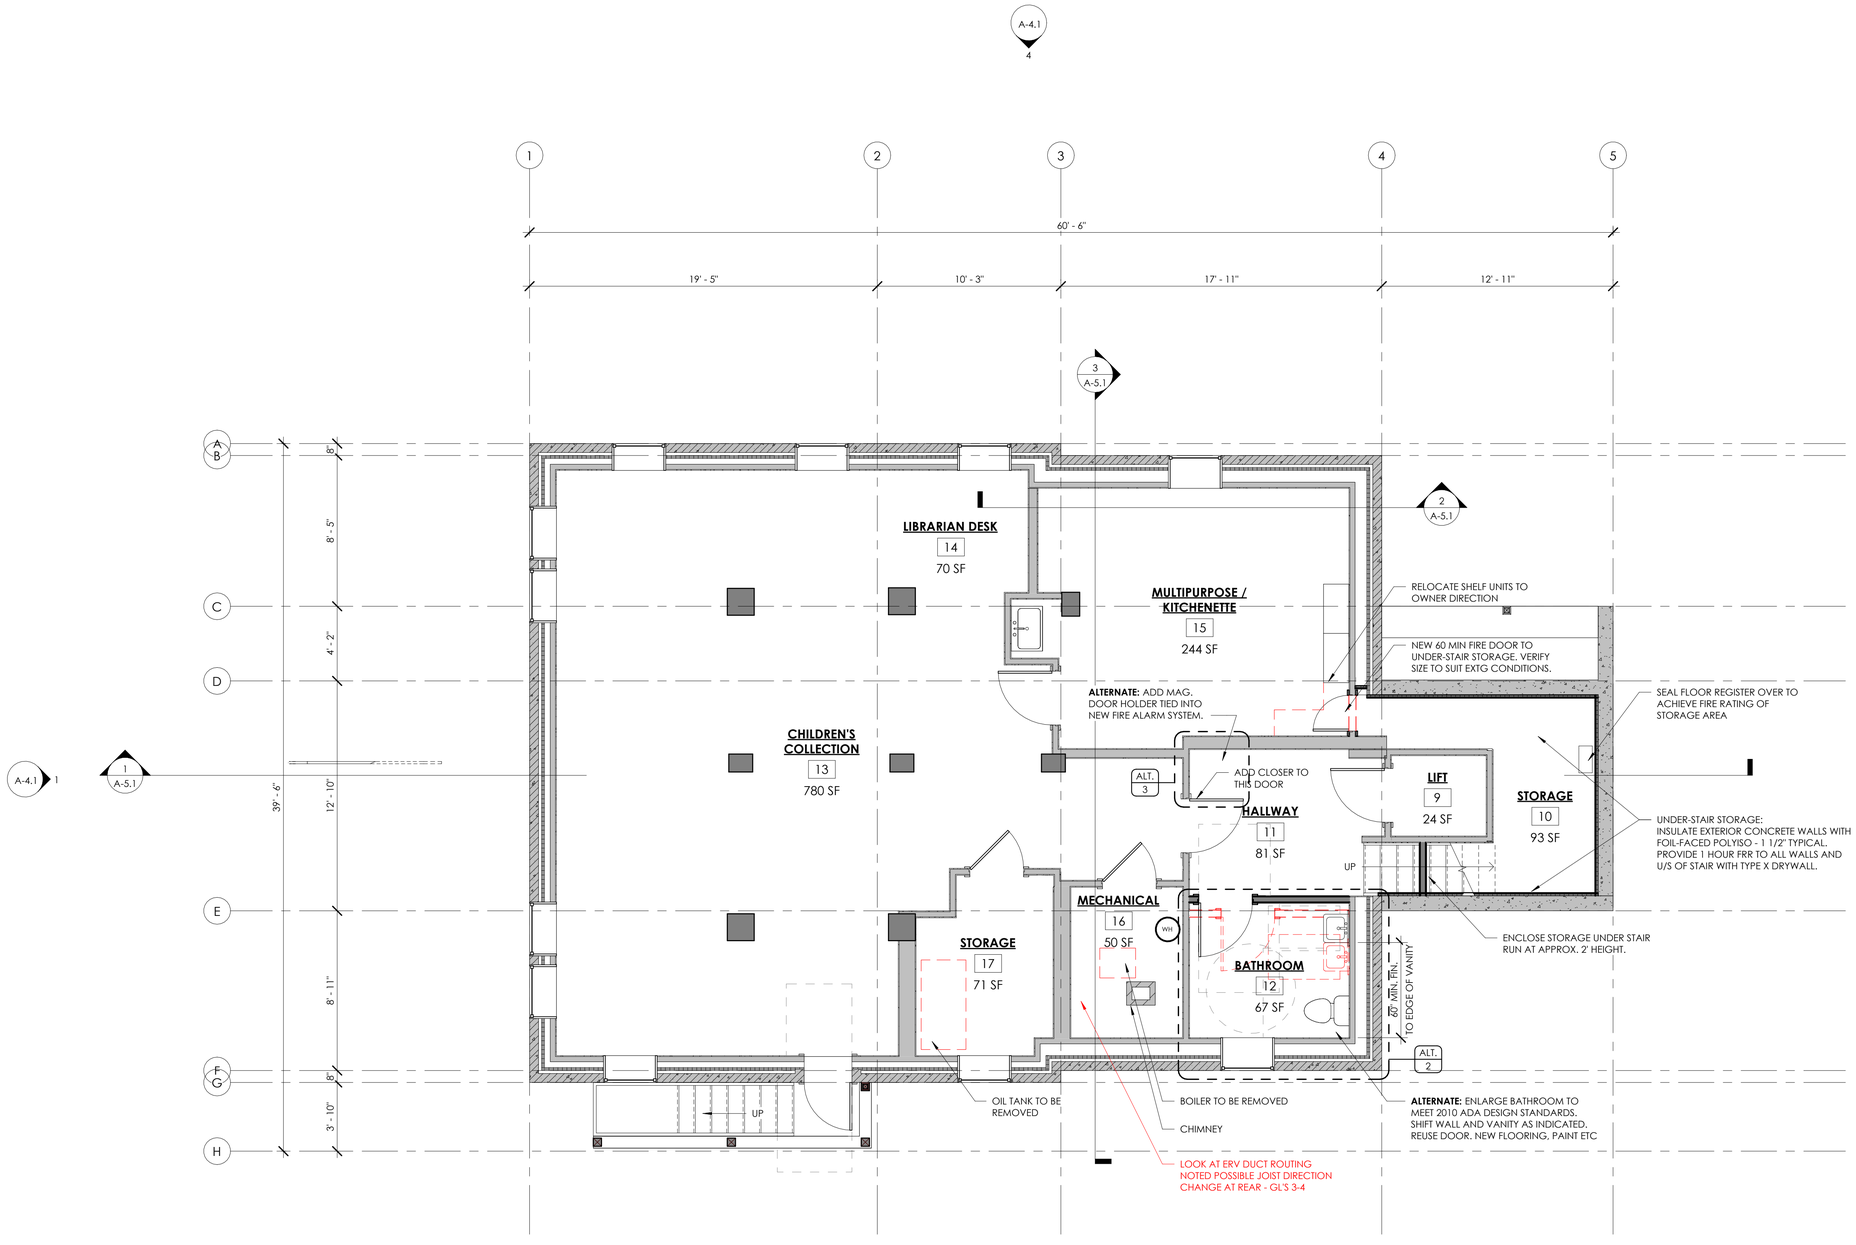


1 Basement Proposed
1/4" = 1'-0"

FLOOR PLAN LEGEND

- EXISTING WALL
- DEMOLISH/REMOVE
- NEW WALL/NEW WALL INFILL

ELEVATION : 0' - 0" = XXX.XX'

1. 0' - 0" = *XXX FLOOR SUBFLOOR*
2. SEE CIVIL DRAWINGS FOR MORE INFORMATION REGARDING SITE ELEVATIONS AND BENCHMARKS.

GENERAL NOTES:

1. VERIFY ALL DIMENSIONS IN FIELD PRIOR TO CONSTRUCTION. NOTIFY ARCHITECT OF DISCREPANCIES.
2. ALL DIMENSIONS TO FACE OF FRAMING U.O.N.

N

0' 2' 4' 8' 12'

VERMONT INTEGRATED
ARCHITECTURE, PC

ANDREA MURRAY, AIA, NCARB, LEED AP
andrea@vermontintegratedarchitecture.com

ASHAR NELSON, AIA, LEED AP
ashar@vermontintegratedarchitecture.com

MEGAN NEDZINSKI, AIA, NCARB, LEED AP, CPHC
megan@vermontintegratedarchitecture.com

P.O. Box 862
Middlebury, VT 05753
802.989.7249

TYPE OF CONSULTANT
First Last
Company
email address
000.000.0000

LICENSED ARCHITECT JAMES ASHAR NELSON NO. 2888 STATE OF VERMONT

DATE ISSUED: 3/19/26
Drawn: EO
Checked: NW

REVISIONS:

BRISTOL ENERGY RESILIENCE PROJECTS

LAWRENCE MEMORIAL LIBRARY

40 North St,
Bristol,
VT 05443

PROPOSED FLOOR PLANS

A-2.1