
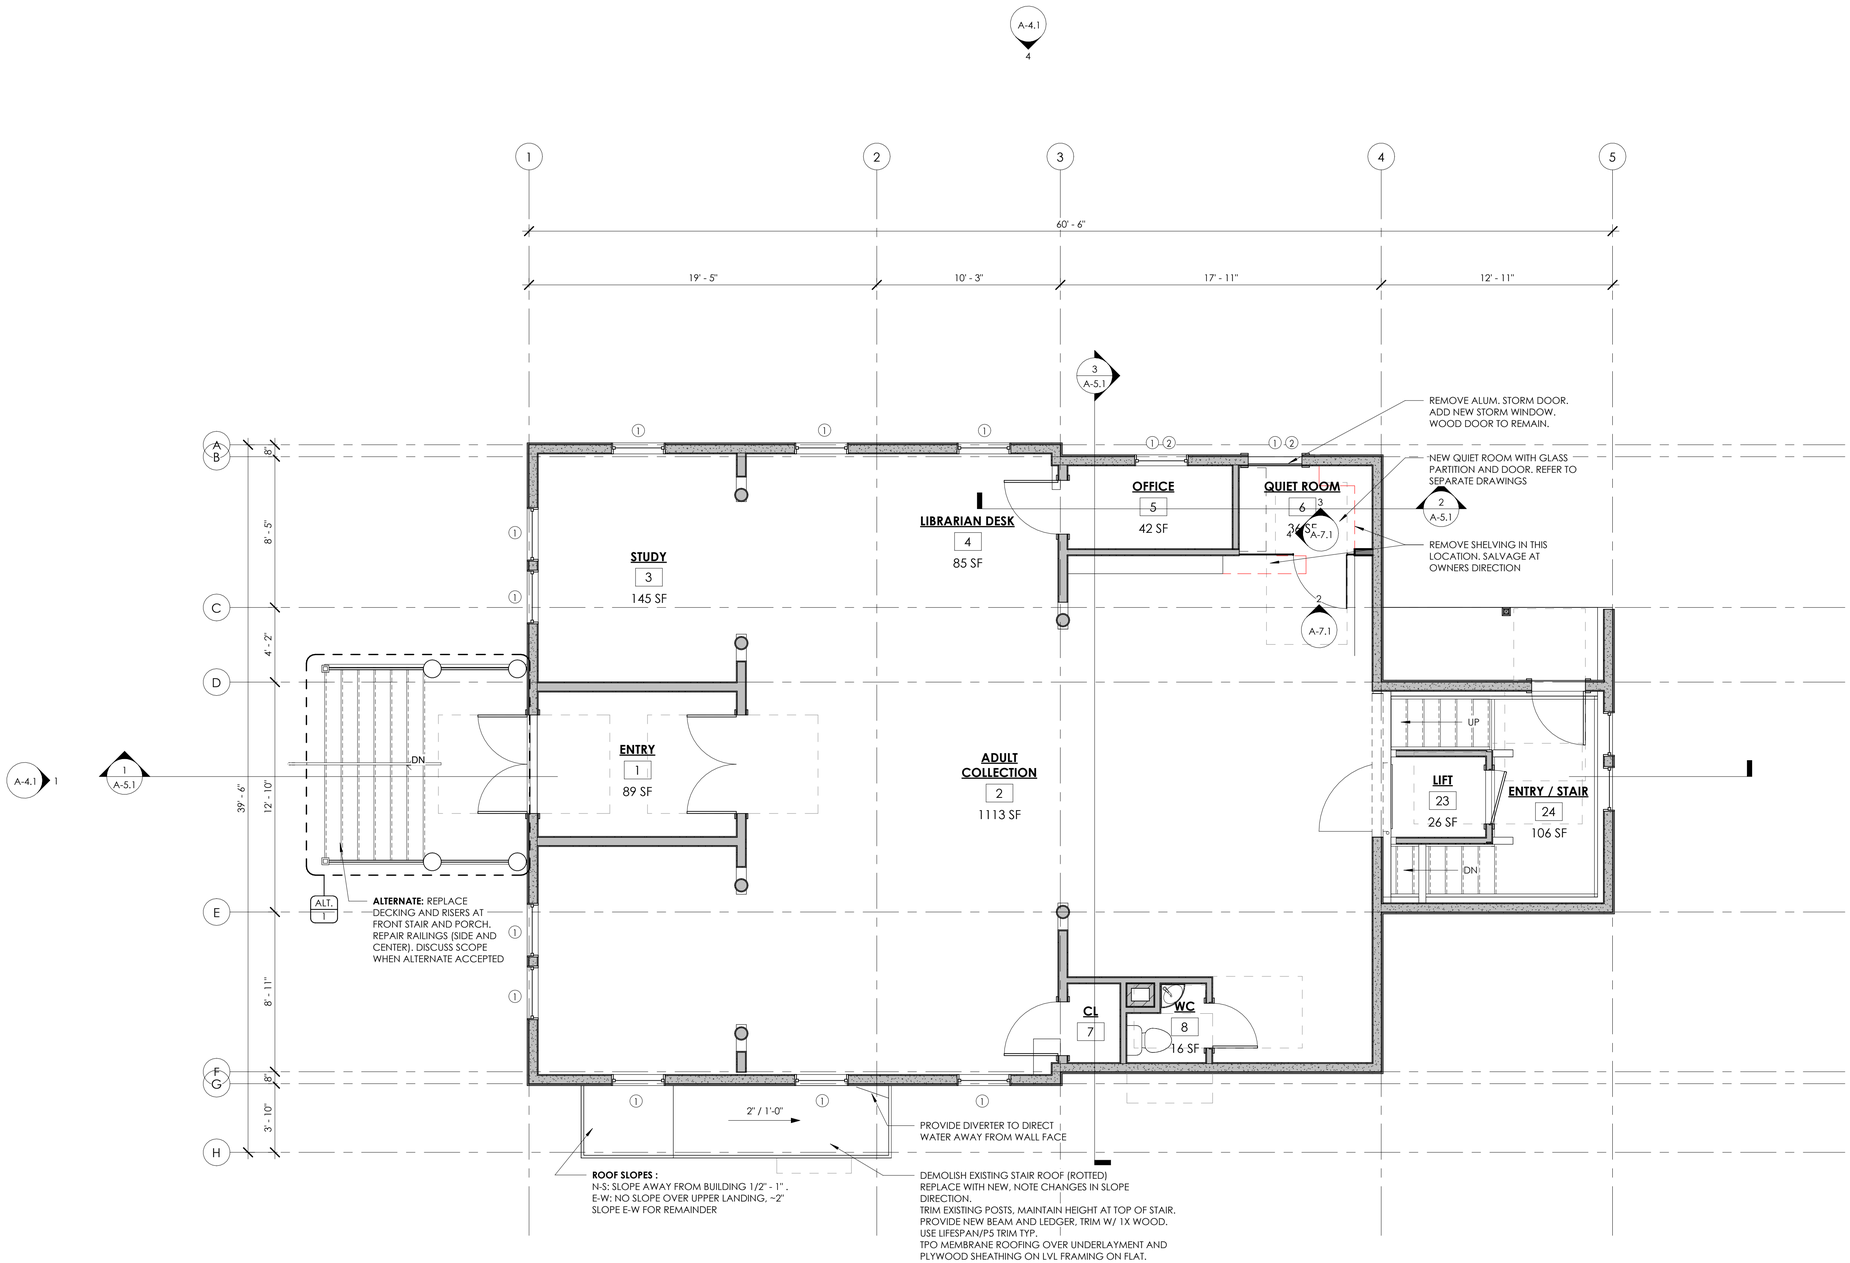


1 First Floor Proposed
1/4" = 1'-0"

2
A-4,1

ENVELOPE UPGRADE NOTES	
NO.	NOTE
1	WEATHER STRIP EXISTING WINDOW/DOOR AT TOP, BOTTOM, AND EDGES. INSPECT AND REPAIR WEIGHT MECHANISMS AS APPLICABLE. SINGLE HUNG OPERATION IS SUFFICIENT, ALLOWING UPPER SASH TO BE AIR SEALED.
2	INSTALL STORM WINDOWS PER SPEC.
3	REPLACE WOOD SILLS WITH STONE OR COMPOSITE SILL TYP. ALL BASEMENT WINDOWS

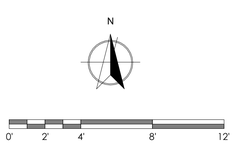

FLOOR PLAN LEGEND

- EXISTING WALL
- DEMOLISH/REMOVE
- NEW WALL/NEW WALL INFILL

ELEVATION : 0' - 0" = XXX.XX'
1. 0' - 0" = *XXX FLOOR SUBFLOOR*
2. SEE CIVIL DRAWINGS FOR MORE INFORMATION REGARDING SITE ELEVATIONS AND BENCHMARKS.

GENERAL NOTES:
1. VERIFY ALL DIMENSIONS IN FIELD PRIOR TO CONSTRUCTION. NOTIFY ARCHITECT OF DISCREPANCIES.
2. ALL DIMENSIONS TO FACE OF FRAMING U.O.N.

VERMONT INTEGRATED
ARCHITECTURE, PC

ANDREA MURRAY, AIA, NCARB, LEED AP
andrea@vermontintegratedarchitecture.com

ASHAR NELSON, AIA, LEED AP
ashar@vermontintegratedarchitecture.com

MEGAN NEDZINSKI, AIA, NCARB, LEED AP, CPHC
megan@vermontintegratedarchitecture.com

P.O. Box 862
Middlebury, VT 05753
802.989.7249

TYPE OF CONSULTANT
First Last
Company
email address
000.000.0000

LICENSED ARCHITECT
ASHAR NELSON
NO. 088
STATE OF VERMONT

DATE ISSUED: 3/19/26
Drawn: EO
Checked: NW

REVISIONS:

BRISTOL ENERGY RESILIENCE PROJECTS

LAWRENCE MEMORIAL LIBRARY

40 North St,
Bristol,
VT 05443

PROPOSED FLOOR PLANS

A-2.2