
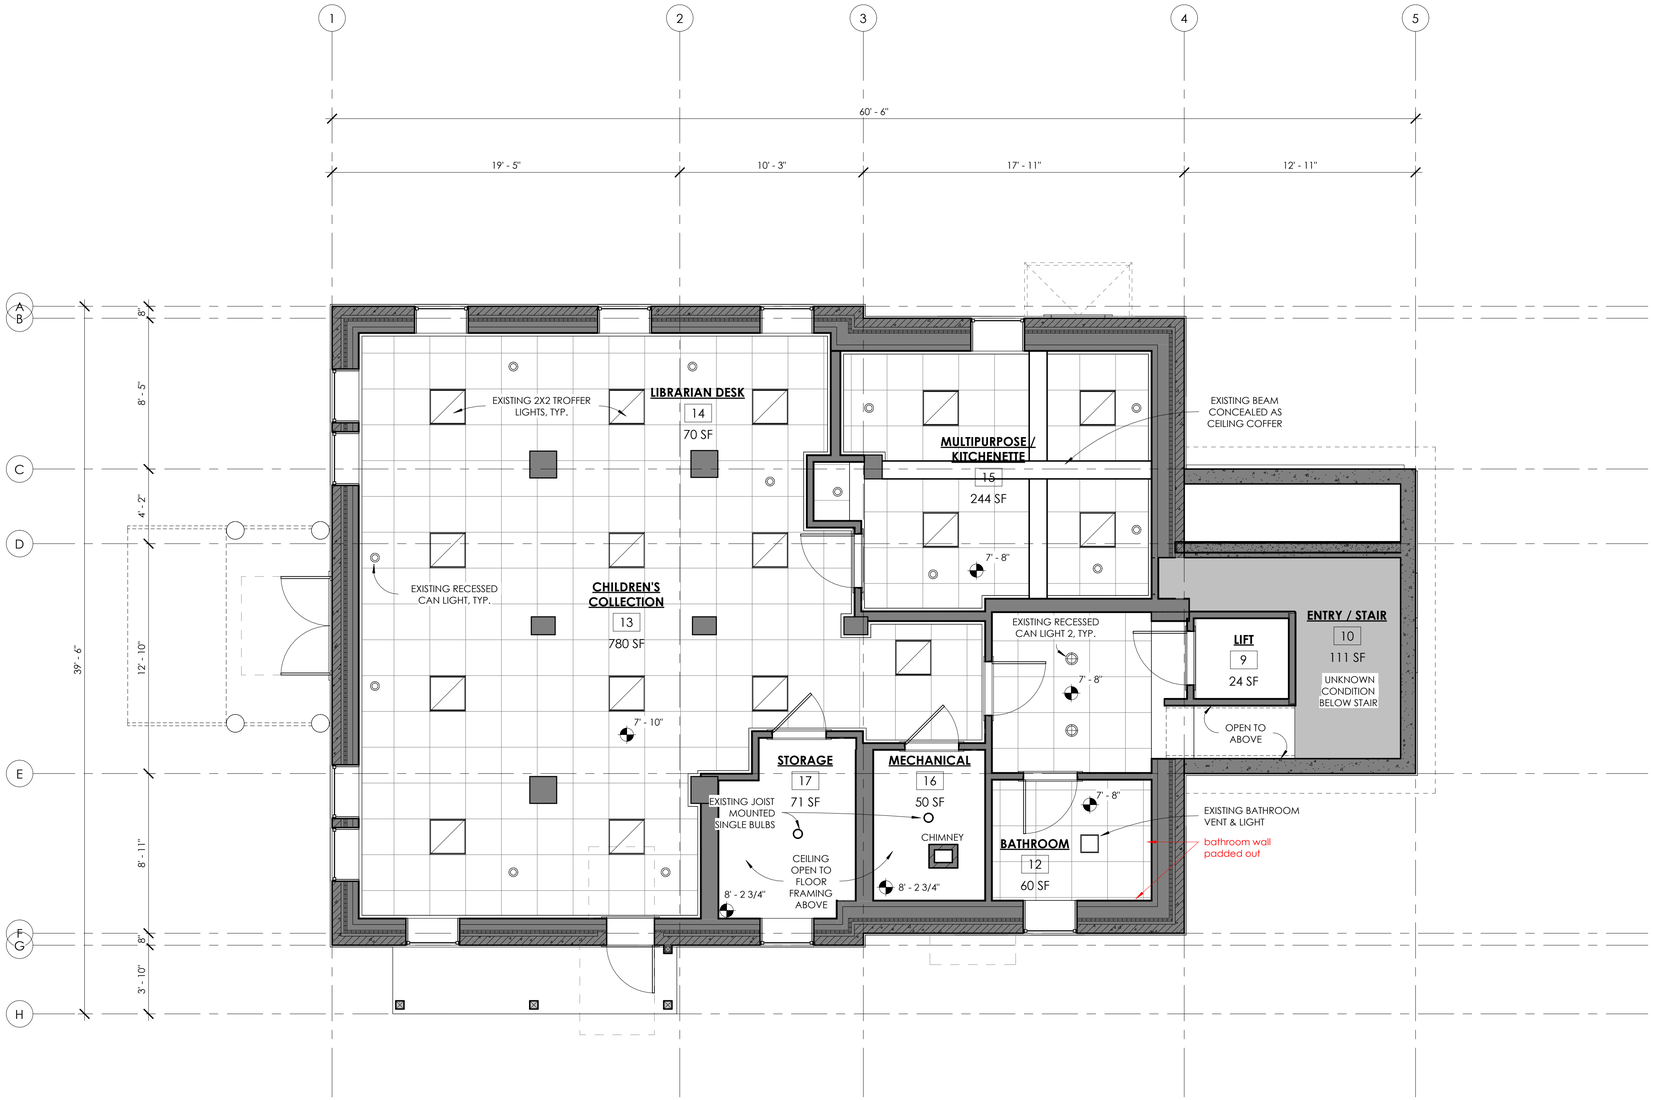


1 Basement Proposed
1/4" = 1'-0"

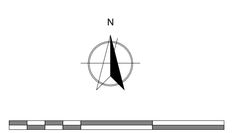

ELEVATION : 0' - 0" = XXX.XX'
1. 0' - 0" = *XXX FLOOR SUBFLOOR*
2. SEE CIVIL DRAWINGS FOR MORE INFORMATION REGARDING SITE ELEVATIONS AND BENCHMARKS.

GENERAL NOTES:
1. VERIFY ALL DIMENSIONS IN FIELD PRIOR TO CONSTRUCTION. NOTIFY ARCHITECT OF DISCREPANCIES.
2. ALL DIMENSIONS TO FACE OF FRAMING U.O.N.

VERMONT INTEGRATED
ARCHITECTURE, PC

ANDREA MURRAY, AIA, NCARB, LEED AP
andrea@vermontintegratedarchitecture.com

ASHAR NELSON, AIA, LEED AP
ashar@vermontintegratedarchitecture.com

MEGAN NEDZINSKI, AIA, NCARB, LEED AP, CPHC
megan@vermontintegratedarchitecture.com

P.O. Box 862
Middlebury, VT 05753
802.989.7249

TYPE OF CONSULTANT
First Last
Company
email address
000.000.0000

LICENSED ARCHITECT
JAMES ASHAR NELSON
NO. 2869
STATE OF VERMONT

DATE ISSUED: 3/19/26
Drawn: EO
Checked: NW

REVISIONS:

BRISTOL ENERGY RESILIENCE PROJECTS

LAWRENCE MEMORIAL LIBRARY

40 North St,
Bristol,
VT 05443

PROPOSED REFLECTED CEILING PLANS

A-3.1