



4 North Elevation Proposed
3/16" = 1'-0"

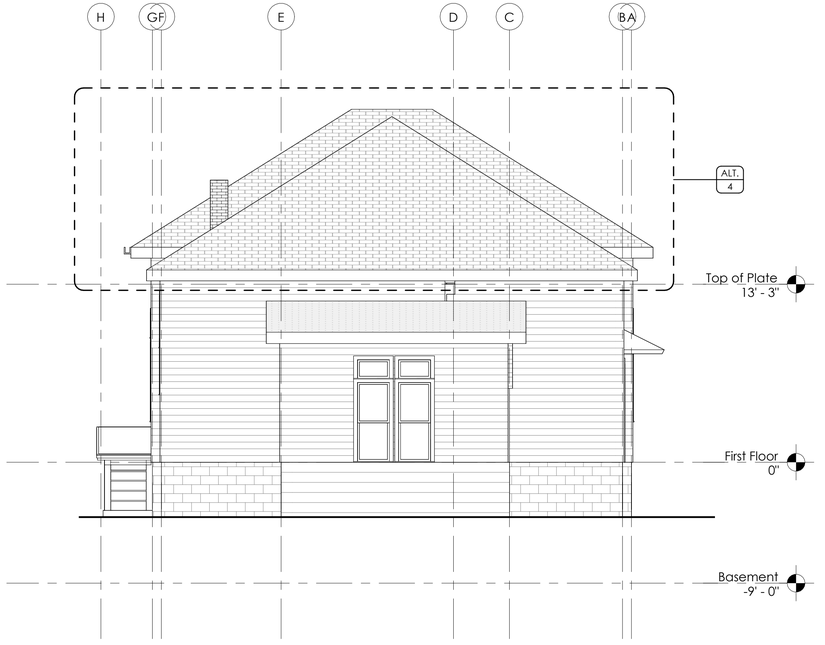


3 East Elevation Proposed
3/16" = 1'-0"

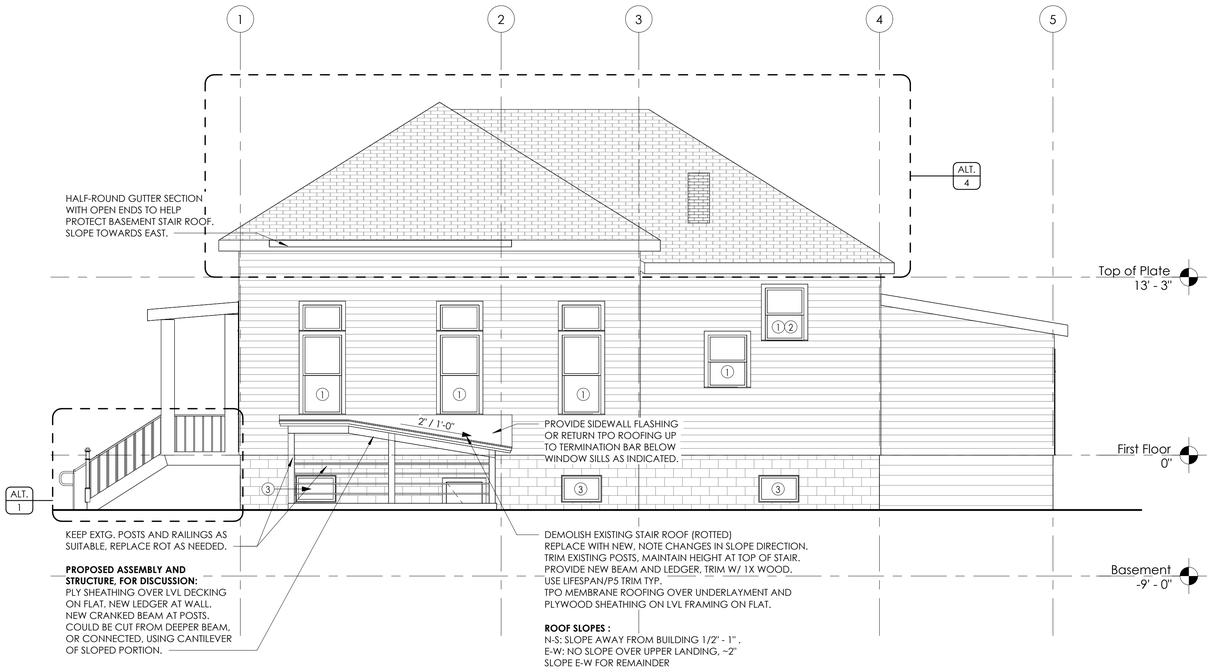

2 South Elevation Proposed
3/16" = 1'-0"

ENVELOPE UPGRADE NOTES	
NO.	NOTE
1	WEATHER STRIP EXISTING WINDOW/DOOR AT TOP, BOTTOM, AND EDGES. INSPECT AND REPAIR WEIGHT MECHANISMS AS APPLICABLE. SINGLE HUNG OPERATION IS SUFFICIENT, ALLOWING UPPER SASH TO BE AIR SEALED.
2	INSTALL STORM WINDOWS PER SPEC.
3	REPLACE WOOD SILLS WITH STONE OR COMPOSITE SILL TYP. ALL BASEMENT WINDOWS

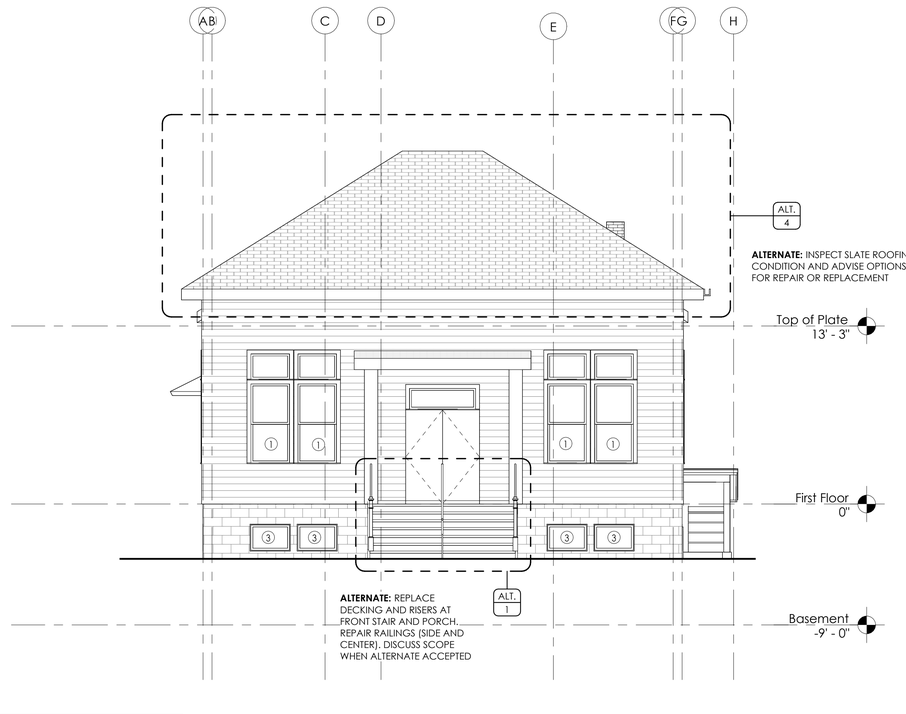

1 West Elevation Proposed
3/16" = 1'-0"

VERMONT INTEGRATED
ARCHITECTURE, PC

ANDREA MURRAY, AIA, NCARB, LEED AP
andrea@vermontintegratedarchitecture.com

ASHAR NELSON, AIA, LEED AP
ashar@vermontintegratedarchitecture.com

MEGAN NEDZINSKI, AIA, NCARB, LEED AP, CPHC
megan@vermontintegratedarchitecture.com

P.O. Box 862
Middlebury, VT 05753
802.989.7249

TYPE OF CONSULTANT
First Last
Company
email address
000.000.0000

LICENSED ARCHITECT
JAMES ASHAR NELSON
NO. 2855
STATE OF VERMONT

DATE ISSUED: 3/19/26
Drawn: EO
Checked: NW

REVISIONS:

BRISTOL ENERGY RESILIENCE PROJECTS

LAWRENCE MEMORIAL LIBRARY

40 North St,
Bristol,
VT 05443

PROPOSED ELEVATIONS

A-4.1