

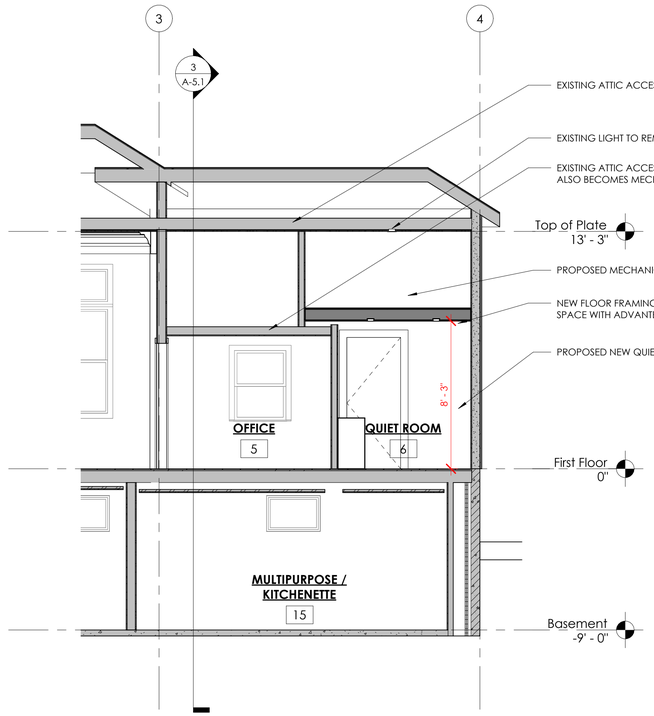


2 Section at Internal Mech Space
1/4" = 1'-0"

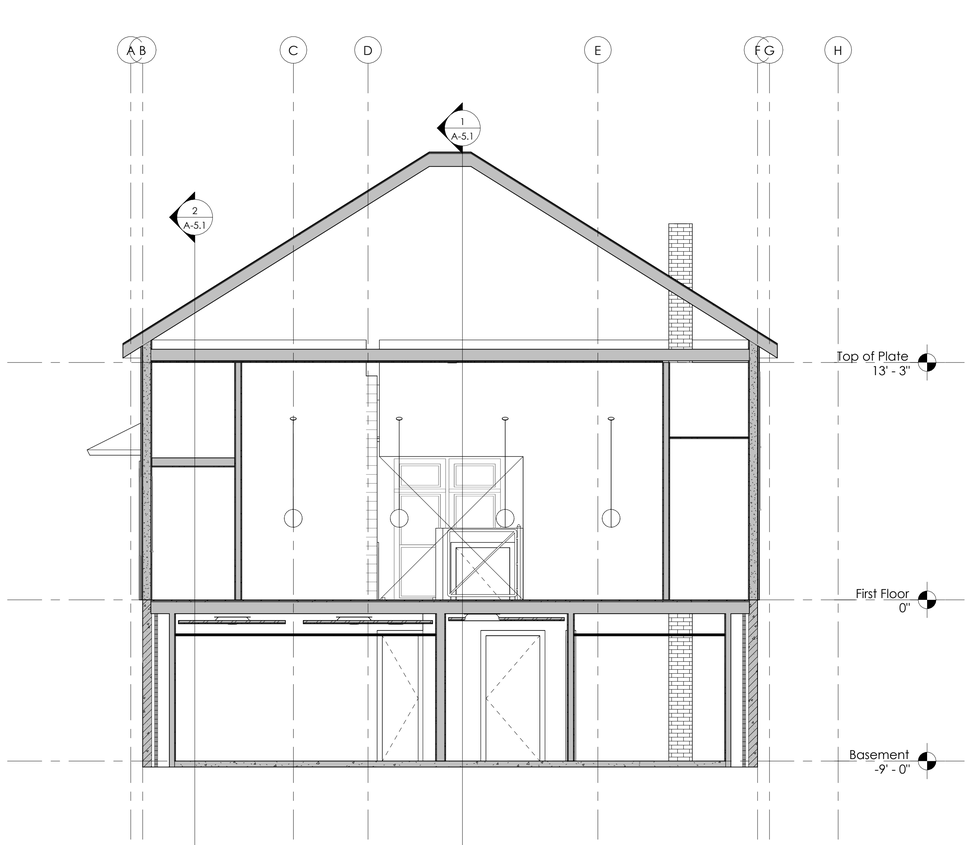

3 Cross Section at Attic Mech. Space
1/4" = 1'-0"

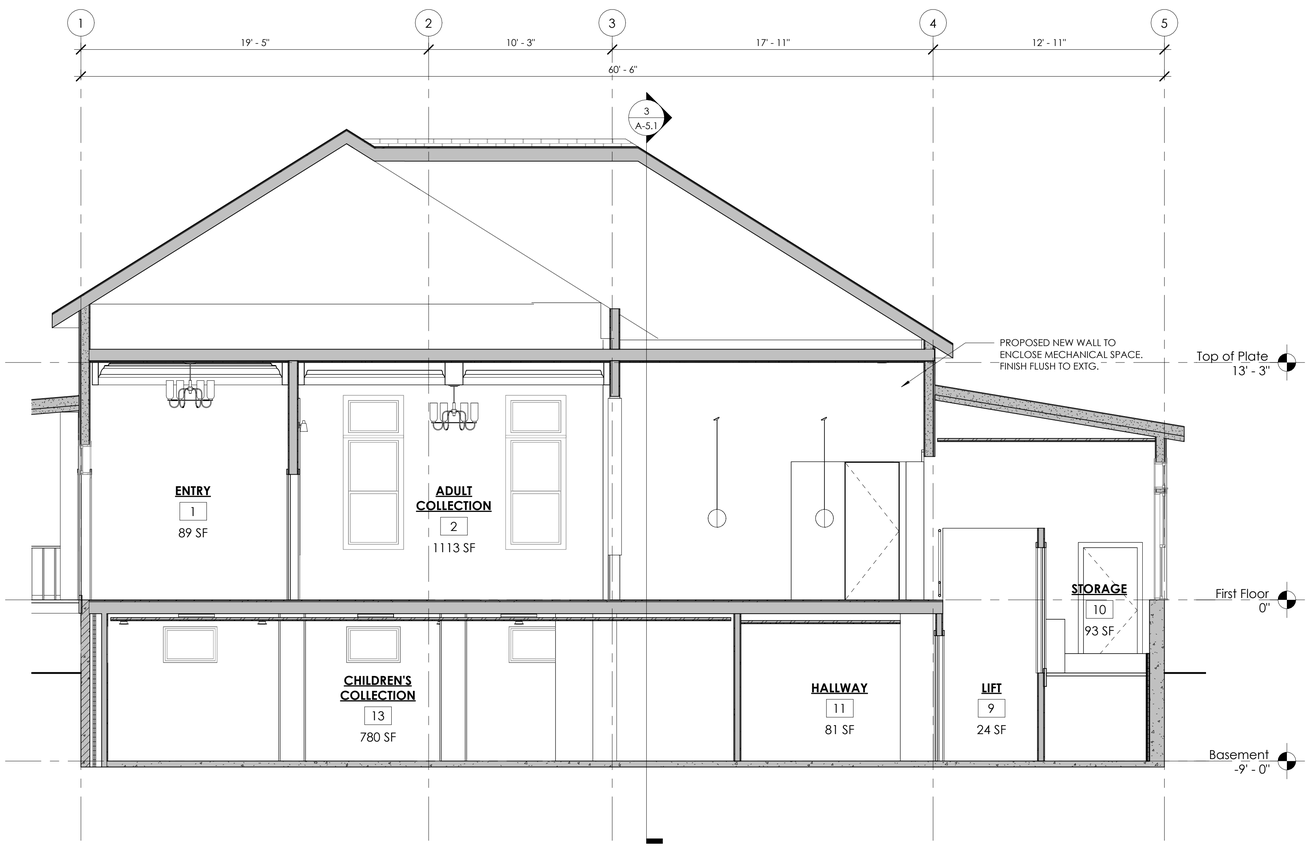

1 Longitudinal Section Proposed
1/4" = 1'-0"

VERMONT INTEGRATED
ARCHITECTURE, PC

ANDREA MURRAY, AIA, NCARB, LEED AP
andrea@vermontintegratedarchitecture.com

ASHAR NELSON, AIA, LEED AP
ashar@vermontintegratedarchitecture.com

MEGAN NEDZINSKI, AIA, NCARB, LEED AP, CPHC
megan@vermontintegratedarchitecture.com

P.O. Box 862
Middlebury, VT 05753
802.989.7249

TYPE OF CONSULTANT
First Last
Company
email address
000.000.0000

LICENSED ARCHITECT
JAMES ASHAR NELSON
NO. 2868
STATE OF VERMONT

DATE ISSUED: 3/19/26
Drawn: EO
Checked: NW

REVISIONS:

BRISTOL ENERGY RESILIENCE PROJECTS

LAWRENCE MEMORIAL LIBRARY

40 North St,
Bristol,
VT 05443

PROPOSED BUILDING SECTION

A-5.1

3/20/2026 4:37:31 PM