

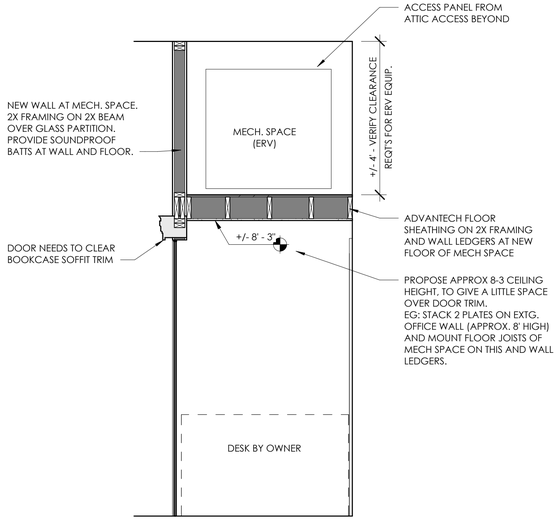



4 Quiet Room - Desk Wall
1/2" = 1'-0"

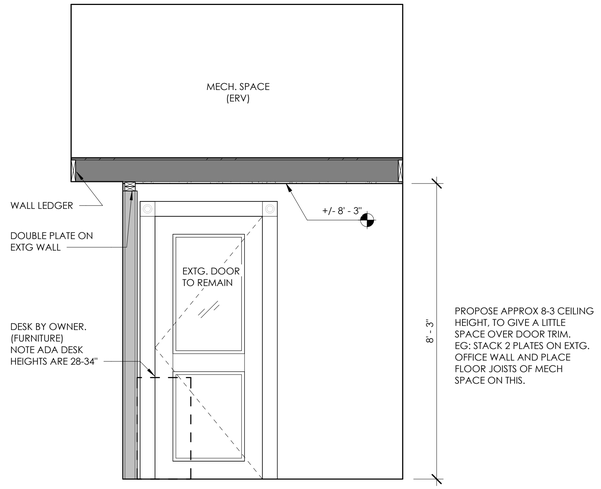

3 Quiet Room - Exterior Wall
1/2" = 1'-0"

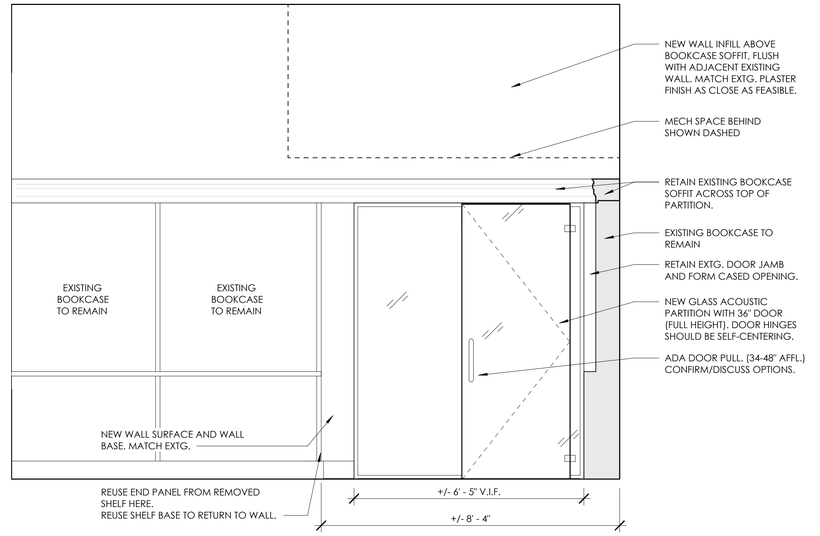

2 Quiet Room - Entry Door & Bookcases
1/2" = 1'-0"

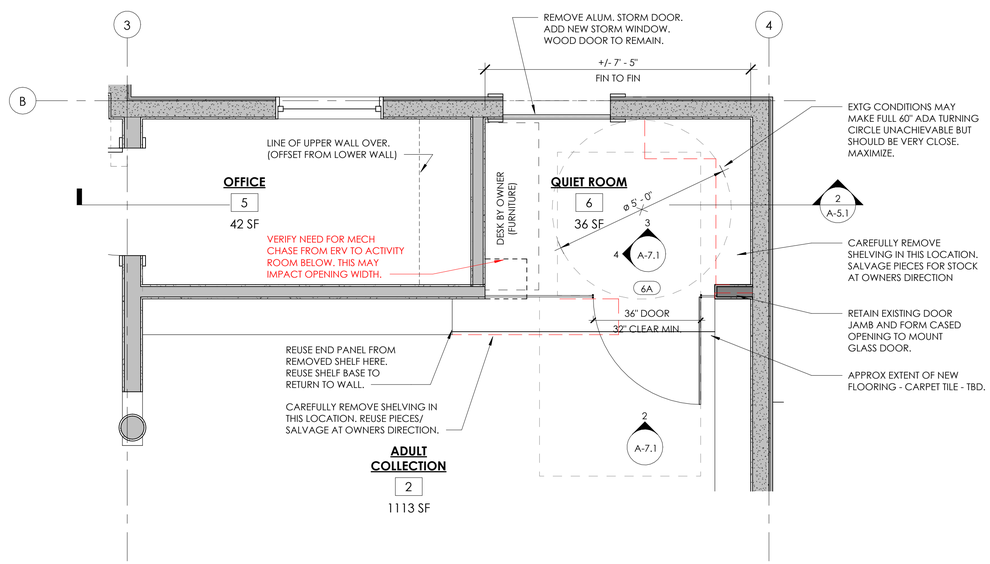

1 Quiet Room - Enlarged Plan
1/2" = 1'-0"

VERMONT INTEGRATED
ARCHITECTURE, PC

ANDREA MURRAY, AIA, NCARB, LEED AP
andrea@vermontintegratedarchitecture.com

ASHAR NELSON, AIA, LEED AP
ashar@vermontintegratedarchitecture.com

MEGAN NEDZINSKI, AIA, NCARB, LEED AP, CPHC
megan@vermontintegratedarchitecture.com

P.O. Box 862
Middlebury, VT 05753
802.989.7249

TYPE OF CONSULTANT
First Last
Company
email address
000.000.0000

LICENSED ARCHITECT JAMES ASHAR NELSON NO. 088 STATE OF VERMONT

DATE ISSUED: 3/19/26
Drawn: GP
Checked: NW

REVISIONS:

BRISTOL ENERGY RESILIENCE PROJECTS

LAWRENCE MEMORIAL LIBRARY

40 North St,
Bristol,
VT 05443

ENLARGED INTERIOR PLAN AND ELEVATIONS

A-7.1